
PRICE SCOPE: only the Nudura ICF formwork and associated accessories are included in our price.
All other structure and information shown is supplied in good faith for coordination only and must be checked by the relevant professional.

QUOTATION - NOT FOR CONSTRUCTION

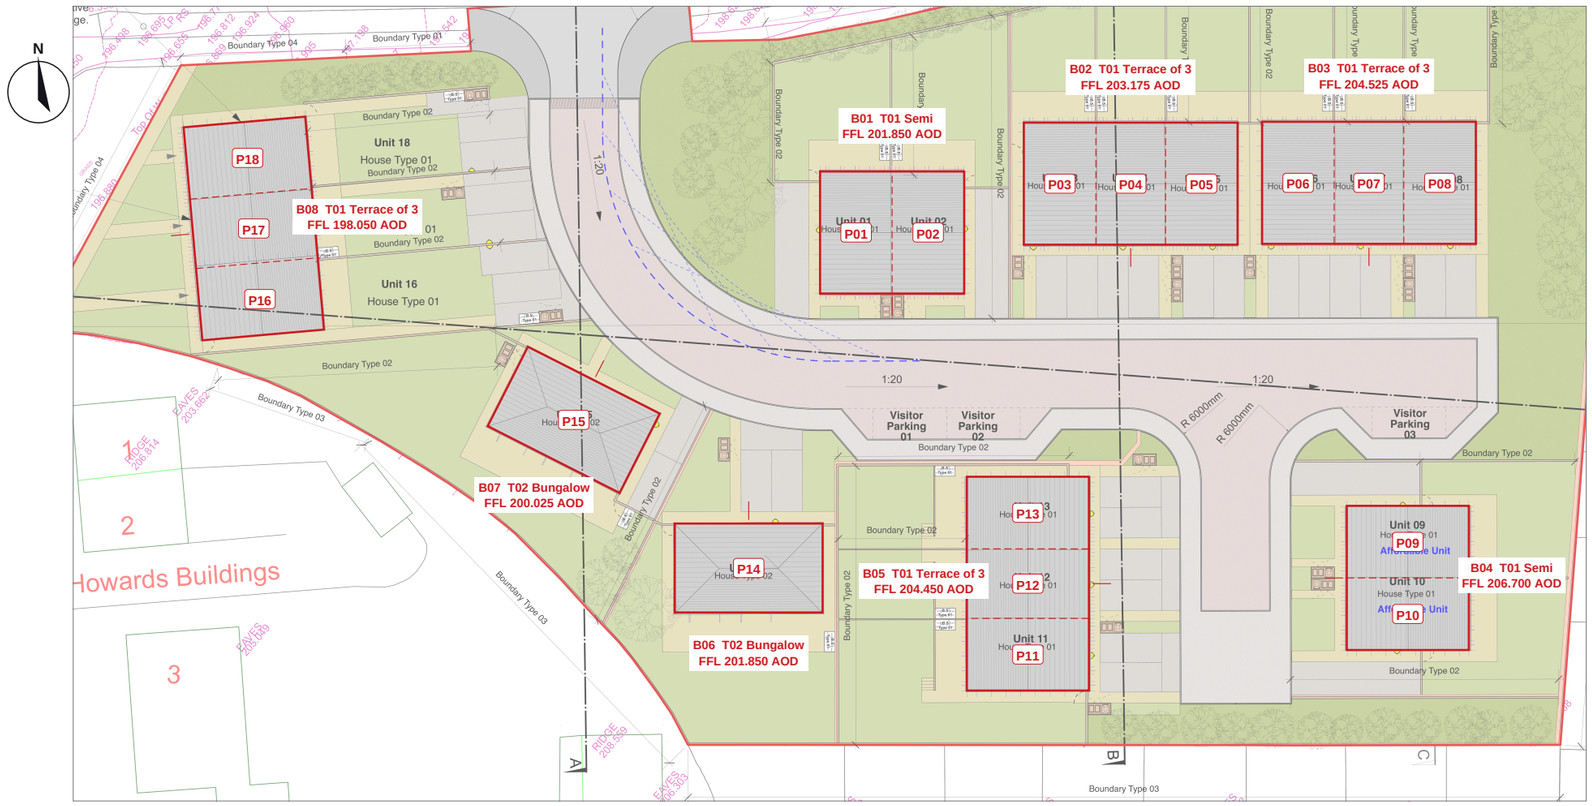

SITE PLAN

Scale 1:500 @ A3 | 24-014-10G base (architect, DRAFT), ICF blocks in red; P = plot number; tick = front door side

0 1 2 3 4 5 6 7 8 9 10 11 12 13 14 15 16 17 18 19 20m

BLOCK SCHEDULE

BLOCKS AND LEVELS

Block	Type	Plots	FFL AOD	Ground AOD	FB crs
B01	T01 Semi	01, 02	201.850	200.86-202.61	2-4
B02	T01 Terrace of 3	03, 04, 05	203.175	202.59-203.81	2-3
B03	T01 Terrace of 3	06, 07, 08	204.525	203.19-205.42	2-5
B04	T01 Semi	09, 10	206.700	206.37-206.74	2-3
B05	T01 Terrace of 3	11, 12, 13	204.450	203.29-205.54	2-4
B06	T02 Bungalow	14	201.850	201.09-202.21	2-4
B07	T02 Bungalow	15	200.025	199.17-200.79	2-4
B08	T01 Terrace of 3	18, 17, 16	198.050	197.14-199.22	2-4

FFL AOD = GF finished floor level (m). Ground = existing ground at the 4 corners (survey, m). FB crs = foundation ICF courses below FFL, 457.2 each (stepped).

BLOCK TYPES

Type	Blocks	Plots
T01 Semi	2	4
T01 Terrace of 3	4	12
T02 Bungalow	2	2
Total	**8**	**18**

NOTES

1. Base: Code L6 Architecture drawing 24-014-10G Site Plan As Proposed (DRAFT), reproduced at 1:500 for location only. Block footprints in red are the Nudura ICF quotation models placed on the 10G roof outlines (external wall faces).
2. Finished floor levels: 10G gives no proposed FFLs (the spot levels are the existing survey). For the quotation each block's GF FFL = MEAN of its four corner existing ground levels + 150, to the nearest 25 mm; the foundation ICF steps on the course grid to follow the ground (schedule and developed elevations on ES26-080-FD-01). Levels to be confirmed by the engineer / architect.
3. Block types: T01 Semi (HT01 x2), T01 Terrace of 3 (HT01 x3), T02 Bungalow (HT02). Left unit as drawn, right unit handed. 18 plots in 8 blocks.
4. Do not scale for setting out: setting out by others from the architect's dimensioned layout.

REVISIONS

REV	DATE	DESCRIPTION
Q01	19.10.26	First issue

Nudura™ BuildEase

CLIENT	PROJECT
Wannop Developments Ltd	Land to Rear of 1-8 Wesley Terrace, Castleside

DRAWING TITLE

SITE PLAN - BLOCKS, PLOTS AND FLOOR LEVELS

10G site plan with the ICF blocks, plot numbers and FFLs

SCALE	SIZE	DATE
1:500	A3	19.10.26
DRAWN	CHECKED	APPROVED
TS		

STATUS	DRAWING No.	REV
QUOTATION	ES26-080-SP-01	Q01

Do not scale. All dimensions in mm. Check all dimensions on site.