

PRICE SCOPE: only the Nudura ICF formwork and associated accessories are included in our price.
All other structure and information shown is supplied in good faith for coordination only and must be checked by the relevant professional.

QUOTATION - NOT FOR CONSTRUCTION


J2 - 5,371 O/A x 253 deep - 38 No. (J1 = 5,383 o/a, same profile)

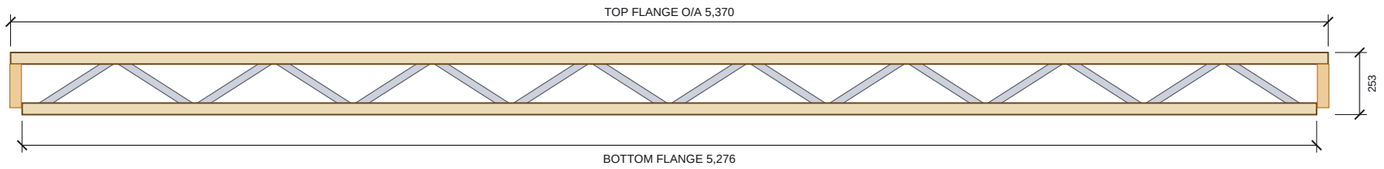

J4 - 4,277 O/A x 253 deep - 14 No. (J3 = 4,289 o/a, same profile)

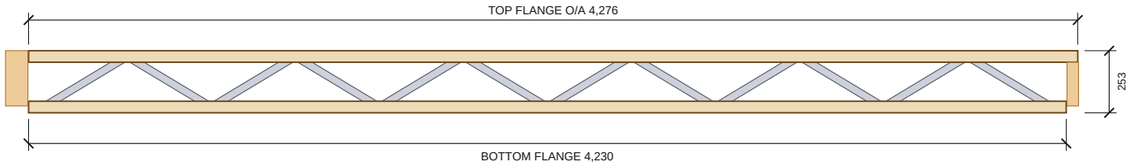

Elevations 1:25 (ledgers / trimmer at each end shown for context)

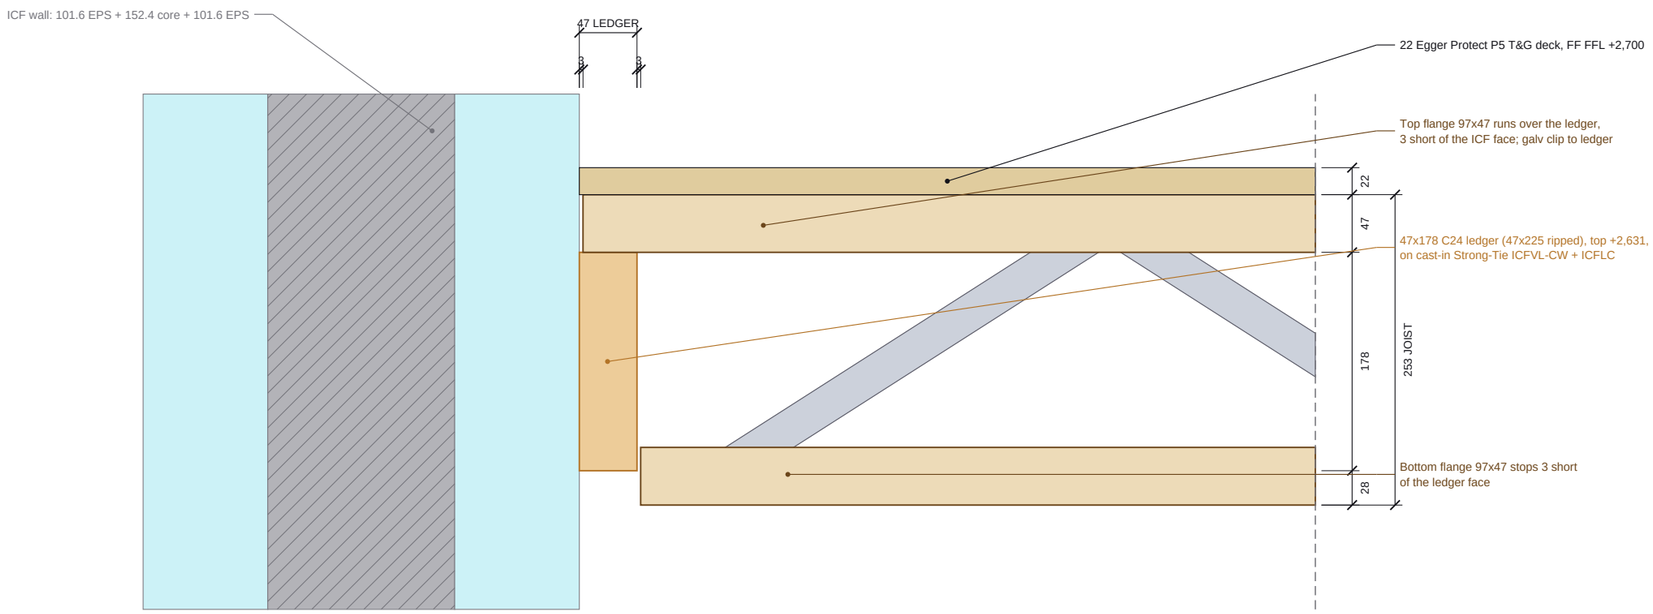

TOP-HUNG BEARING ON CUT-DOWN LEDGER

Scale 1:5 | typical, gable and party ends

JOIST TYPES

JOIST SCHEDULE

Type	O/A	Bottom	Depth	Flanges	Qty
J1	5,383	5,289	253	97x47	19
J2	5,371	5,277	253	97x47	38
J3	4,289	4,242	253	97x47	7
J4	4,277	4,230	253	97x47	14
				Total	**78**

Qty = all units of the block. PS10 equivalent, for supplier quote.

WHERE USED

Type	Location
J1	gable / party to party, top-hung; U2; 4 in doubled pairs
J2	gable / party to party, top-hung; U1, U3; 8 in doubled pairs
J3	trimmed, hung off the stair trimmer; U2
J4	trimmed, hung off the stair trimmer; U1, U3

NOTES

1. FOR SUPPLIER QUOTE: 253 deep metal-web joists, e.g. Posi-Joist / Easi-Joist PS10 equivalent, 97 x 47 C24 (or stress-graded) flanges with galvanised V-web plates. The supplier designs the joists for the stated loads and confirms depth, web layout and spacing.
2. Loads (to be confirmed by the supplier): domestic floor, imposed 1.5 kN/m2 + lightweight stud partitions over, 22 Egger Protect P5 deck, plasterboard ceiling under. 400 c/c, span gable to party wall.
3. Top-hung bearing at both ends: top flange runs over the 47 x 178 C24 ledger to 3 short of the ICF face; bottom flange stops 3 short of the ledger. Galv top-chord restraint clip nailed to the ledger at each end. Trimmed joists: face-fix hangers off the stair well trimmer at one end.
4. Web pattern shown is indicative (from the quotation model); webs at the supplier's standard pitch.

REVISIONS

REV	DATE	DESCRIPTION
Q01	19.10.26	First issue

Nudura™ BuildEase

CLIENT	PROJECT
Wannop Developments Ltd	Land to Rear of 1-8 Wesley Terrace, Castleside

DRAWING TITLE
T01 TERRACE OF 3 - FLOOR JOIST PROFILES

Metal-web joist profiles for supplier quotation

SCALE	SIZE	DATE
1:25 / 1:5	A3	19.10.26
DRAWN	**CHECKED**	**APPROVED**
TS		

STATUS	DRAWING No.	REV
QUOTATION	ES26-080-FL-04	Q01

Do not scale. All dimensions in mm. Check all dimensions on site.