
PRICE SCOPE: only the Nudura ICF formwork and associated accessories are included in our price.
All other structure and information shown is supplied in good faith for coordination only and must be checked by the relevant professional.

QUOTATION - NOT FOR CONSTRUCTION

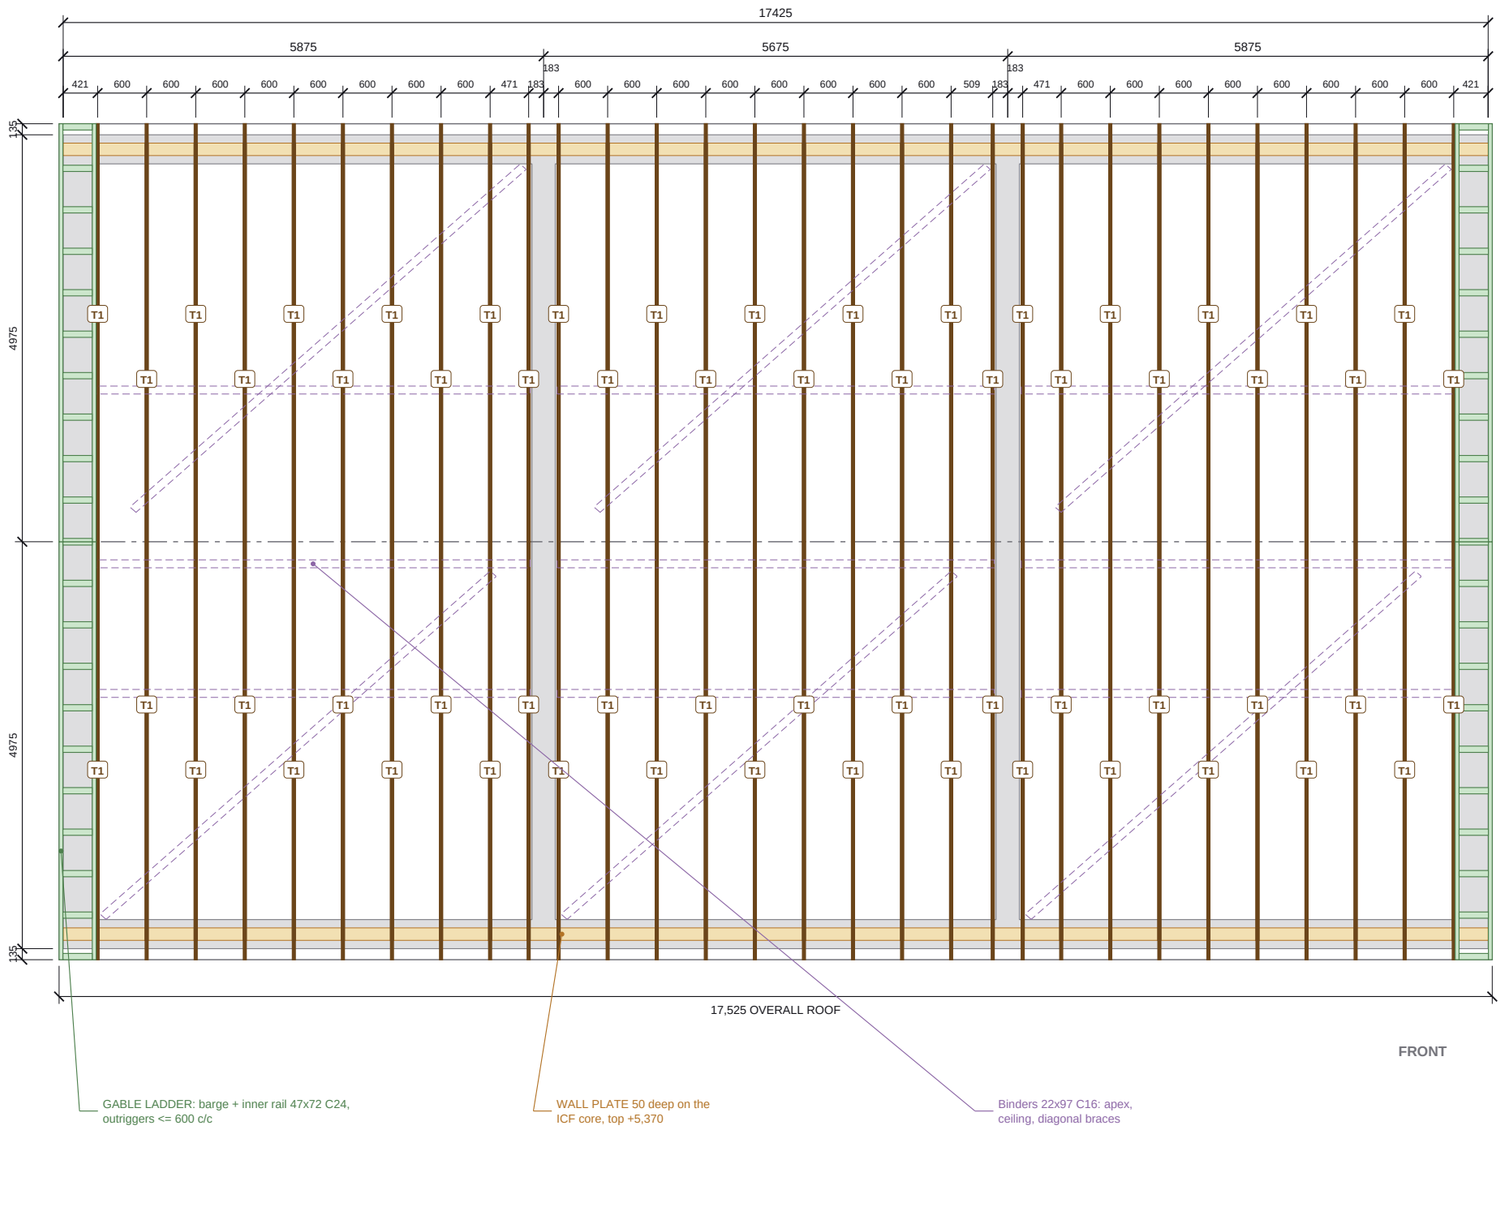

Trussed rafter (type T)
Wall plate on the ICF core
Gable ladder
ICF walls (outline)
Binder / diagonal brace

0 1 2 3 4 5m

ROOF STRUCTURE PLAN

Scale 1:75 @ A3 | Plan on the roof structure, tiles / battens / membrane omitted

ROOF STRUCTURE SCHEDULES

TRUSS SCHEDULE

Type	Description	Bottom chord	Top chord	Qty
T1	Fink (W) 30 deg, duo-pitch	9,747	35x120 TR26	30
	Total trusses			**30**

Profiles, spans, rise and member sizes on ES26-080-RF-04.

LOOSE ROOF TIMBER

Item	Section	Length	Qty
Barge (gable ladder outer rail)	47x72 C24	5,901	4
Binder / diagonal brace	22x97 C16	6,788	6
Binder / diagonal brace	22x97 C16	5,343	3
Binder / diagonal brace	22x97 C16	5,306	6
Gable ladder inner rail	47x72 C24	5,901	4
Ladder outrigger	47x72 C24	358	44

ROOF METALWORK

Item	Qty
Gable restraint strap 30 x 5 (HES)	12
Truss clip to plate (TCP38)	60

NOTES

1. Roof trusses, gable ladders, binders and metalwork as modelled for the quotation (TLS roof framer). The truss manufacturer designs the trusses and the bracing to BS EN 1995-1-1 / BS 5268-3 and confirms the spacing, member sizes and metalwork; this layout is for pricing only.
2. 3 roof bays (one per dwelling, party edge on the party wall core faces): 30 No. Fink trusses at 600 c/c (closing bay 471) set out from the gable / party wall, 30 deg, on a 50 deep timber wall plate bedded on the ICF core of the front and rear walls, plate top +5,370 above GF FFL (eaves walls flat at +5,320).
3. Gable ends: gable ladders (barge + inner rail + outriggers <= 600 c/c), HES restraint straps <= 2 m c/c. Party walls carried up to 50 below the top of the rafters (fire stop by others).
4. Truss clips TCP38 at every bearing. All levels above GF FFL. Dimensions in mm.

REVISIONS

REV	DATE	DESCRIPTION
Q01	19.10.26	First issue

Nudura™ BuildEase

CLIENT	PROJECT
Wannop Developments Ltd	Land to Rear of 1-8 Wesley Terrace, Castleside

DRAWING TITLE
T01 TERRACE OF 3 - ROOF TRUSS LAYOUT

Fink trusses, gable ladders, binders, wall plates

SCALE	SIZE	DATE
AS SHOWN	A3	19.10.26
DRAWN	CHECKED	APPROVED
TS		

STATUS	DRAWING No.	REV
QUOTATION	ES26-080-RF-03	Q01

Do not scale. All dimensions in mm. Check all dimensions on site.