
PRICE SCOPE: only the Nudura ICF formwork and associated accessories are included in our price. All other structure and information shown is supplied in good faith for coordination only and must be checked by the relevant professional.

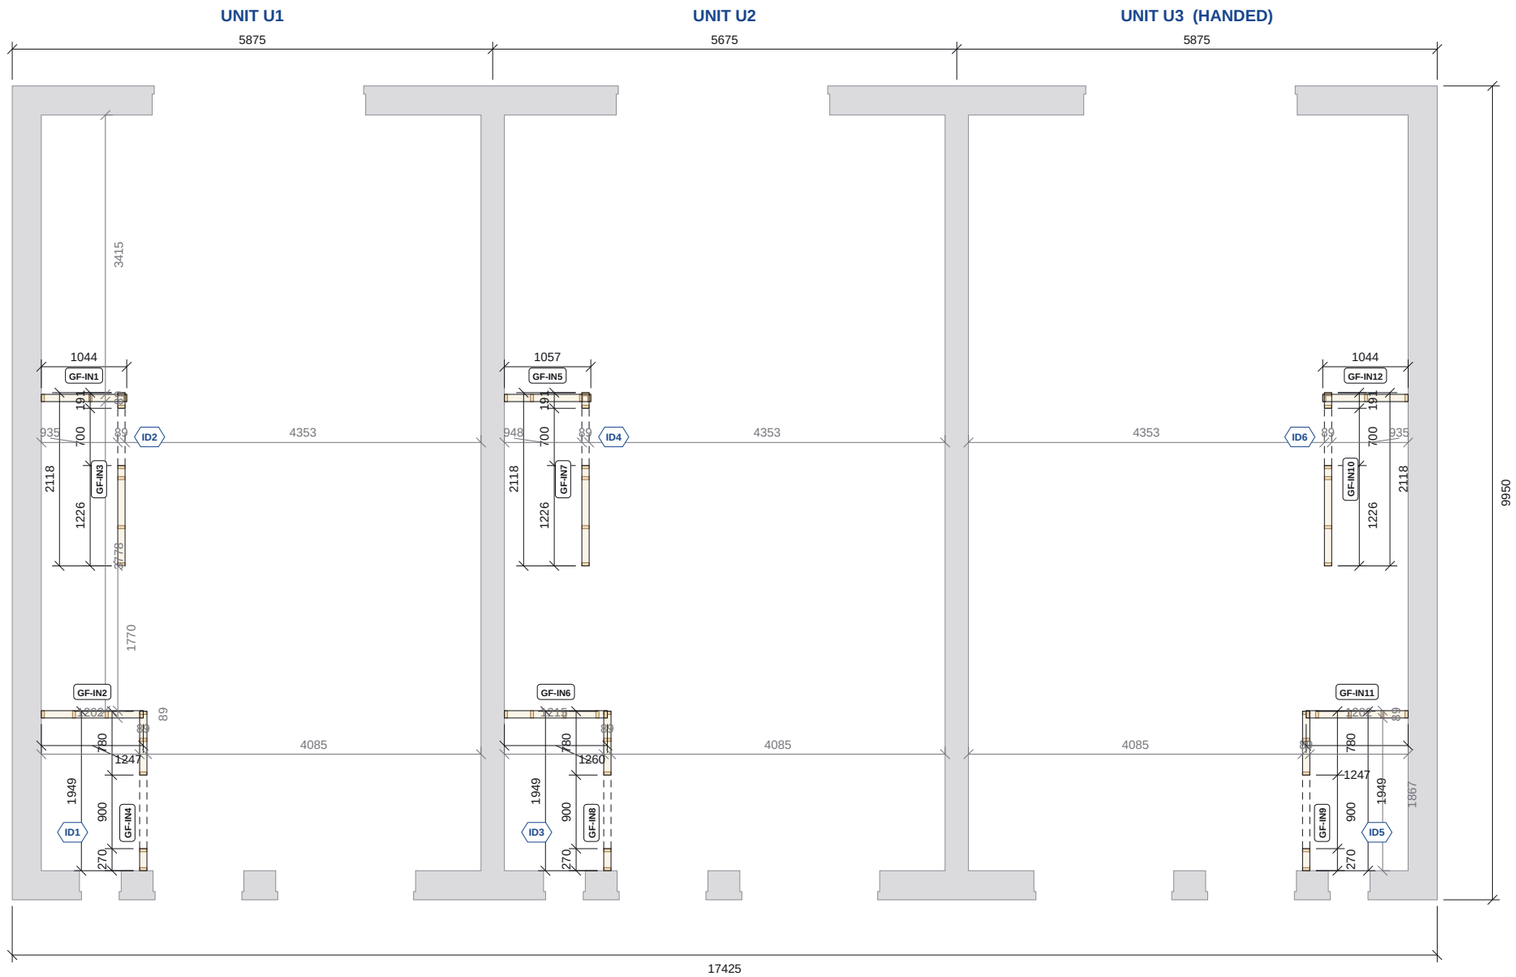

GROUND FLOOR TIMBER PARTITIONS PLAN

Scale 1:75 @ A3 | Plan cut at 1200 above floor level

Partition panel, studs cut at plan level | Panel joint | Nudura ICF shell (context only) | Door opening, head over

0 1 2 3 4 5m

QUOTATION - NOT FOR CONSTRUCTION

Do not scale. All dimensions in mm. Check all dimensions on site.

GROUND FLOOR SCHEDULES

PARTITION SCHEDULE

Panel	Unit	Studs	Use	Length	Doors
GF-IN1	U1	38x89 C16 @600	partition	1044	-
GF-IN2	U1	38x89 C16 @400	bathroom	1247	-
GF-IN3	U1	38x89 C16 @600	partition	2118	ID2
GF-IN4	U1	38x89 C16 @400	bathroom	1949	ID1
GF-IN5	U2	38x89 C16 @600	partition	1057	-
GF-IN6	U2	38x89 C16 @400	bathroom	1260	-
GF-IN7	U2	38x89 C16 @600	partition	2118	ID4
GF-IN8	U2	38x89 C16 @400	bathroom	1949	ID3
GF-IN9	U3	38x89 C16 @400	bathroom	1949	ID5
GF-IN10	U3	38x89 C16 @600	partition	2118	ID6
GF-IN11	U3	38x89 C16 @400	bathroom	1247	-
GF-IN12	U3	38x89 C16 @600	partition	1044	-

Length = panel length along the wall (mm). Head and bottom rails as the studs. Bathroom walls at 400 centres for pattressing; riser boxing 38x47.

DOOR OPENING SCHEDULE

Label	Width	Height	Head	Label	Width	Height	Head
ID1	900	2100	2100	ID4	700	2100	2100
ID2	700	2100	2100	ID5	900	2100	2100
ID3	900	2100	2100	ID6	700	2100	2100

Structural opening sizes. Head level above underside of the bottom rail.

PARTITION TIMBER (THIS FLOOR, ALL UNITS)

Section	Pieces	Run m	4.8m lengths
38x89 C16	159	193.8	43

Studs, rails and noggins from the model. Order lengths = run / 4.8m +5%, not cut-optimised.

NOTES

1. Internal partitions only, non-load-bearing: 38x89 C16 studs at 600 centres with 38x89 C16 head and bottom rails; bathroom walls 38x89 C16 at 400 centres for pattressing; service riser boxing 38x47 C16 at 600. Panel marks refer to the partition schedule.
2. External, party and core walls are Nudura ICF (grey), shown for context only: read with the ICF drawings. Partitions are set out from the ICF internal face and adjacent partitions (grey set-out strings).
3. Door openings are structural opening sizes. Head level above underside of the bottom rail.
4. All units of the block shown (U1 left, seen from the front); the right-hand unit is handed. Dimensions to timber frame faces. Check all dimensions on site.

REVISIONS

REV	DATE	DESCRIPTION
Q01	19.10.26	First issue

Nudura™ BuildEase

CLIENT	PROJECT
Wannop Developments Ltd	Land to Rear of 1-8 Wesley Terrace, Castleside

DRAWING TITLE

T01 TERRACE OF 3 - GROUND FLOOR TIMBER PARTITIONS

Internal stud partitions, panels and door openings

SCALE	SIZE	DATE
1:75	A3	19.10.26
DRAWN	CHECKED	APPROVED
TS		

STATUS	DRAWING No.	REV
QUOTATION	ES26-080-TF-03	Q01